


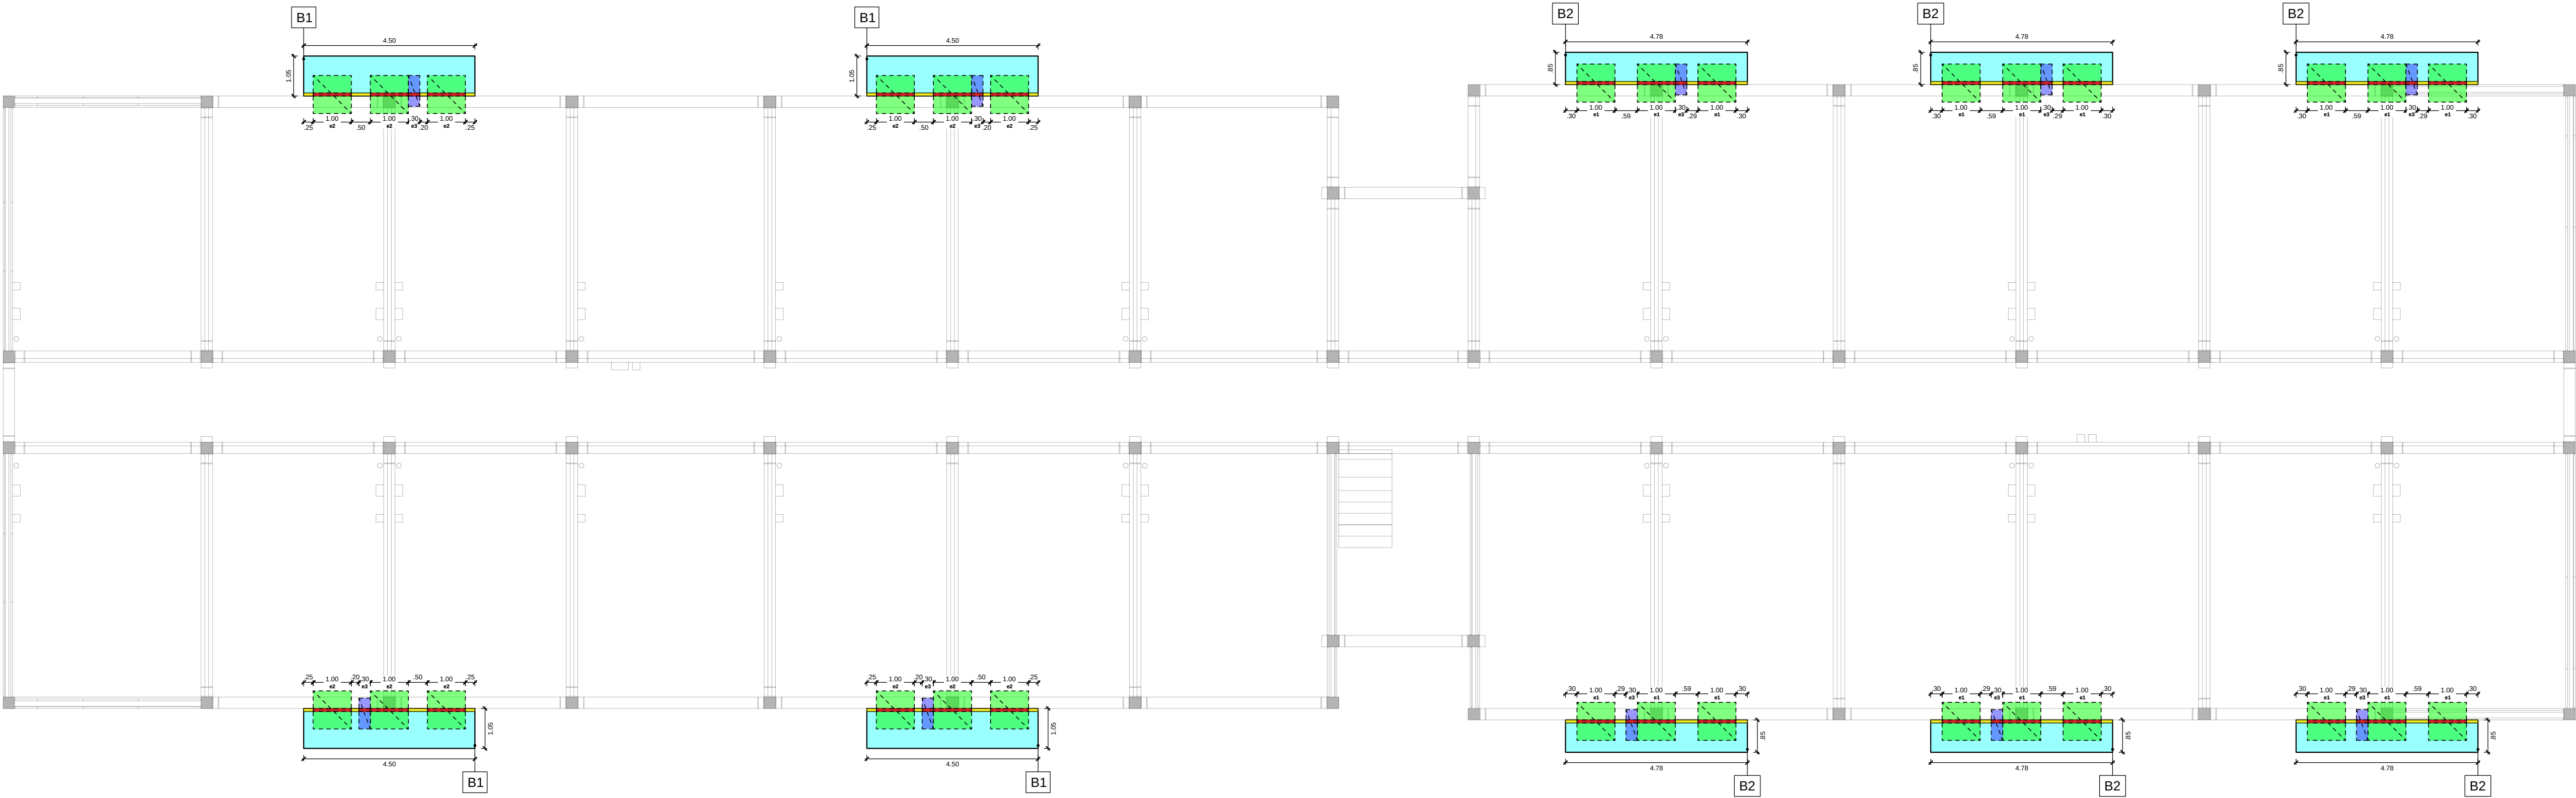

Megjegyzések:

1. Az elemek beépítése kizárólag a felelős statikus tervező részbeni jóváhagyása mellett történhet. Az elemek teherbíróssága a katalógusban megtalálható. A feltüntetett teherbírósságok C25/30-as betonminőségűek lehetnek.

2. A vasbeton szerkezeti elemek nem kerültek felülvizsgálatra. Azok megfelelő vasalással történő ellátása a statikus tervező feladata. A vasbeton szerkezeti elemek méretezése során a hővezetési ellenállás, az elemek hatását figyelembe kell venni.

3. Az elemek beépítésénél a megrendelőt ellenőrizni kell. A megrendelőssel az ajánlatban bemutatott műszaki megoldást elfogadják. Ezzel egyetemben a méreteket ellenőrizni szükséges.

4. Az ajánlat csak az összes melléklettel együtt érvényes.

5. A sárgával jelölt helyekre EBEA-ZS SW80 EI120 vagy egyenértékű szigetelőelem beépítése szükséges!

Termék: EBEA	Építési típus: Munkásszál	Lap: M=1:100
Verzió: R00	Építési cím: Nyíregyháza	Dátum: 06.30.2026
	Szállító: Takács Cédő	Projektazonosító: HU2317
	kezelő: kezelő	Tervező: S1