


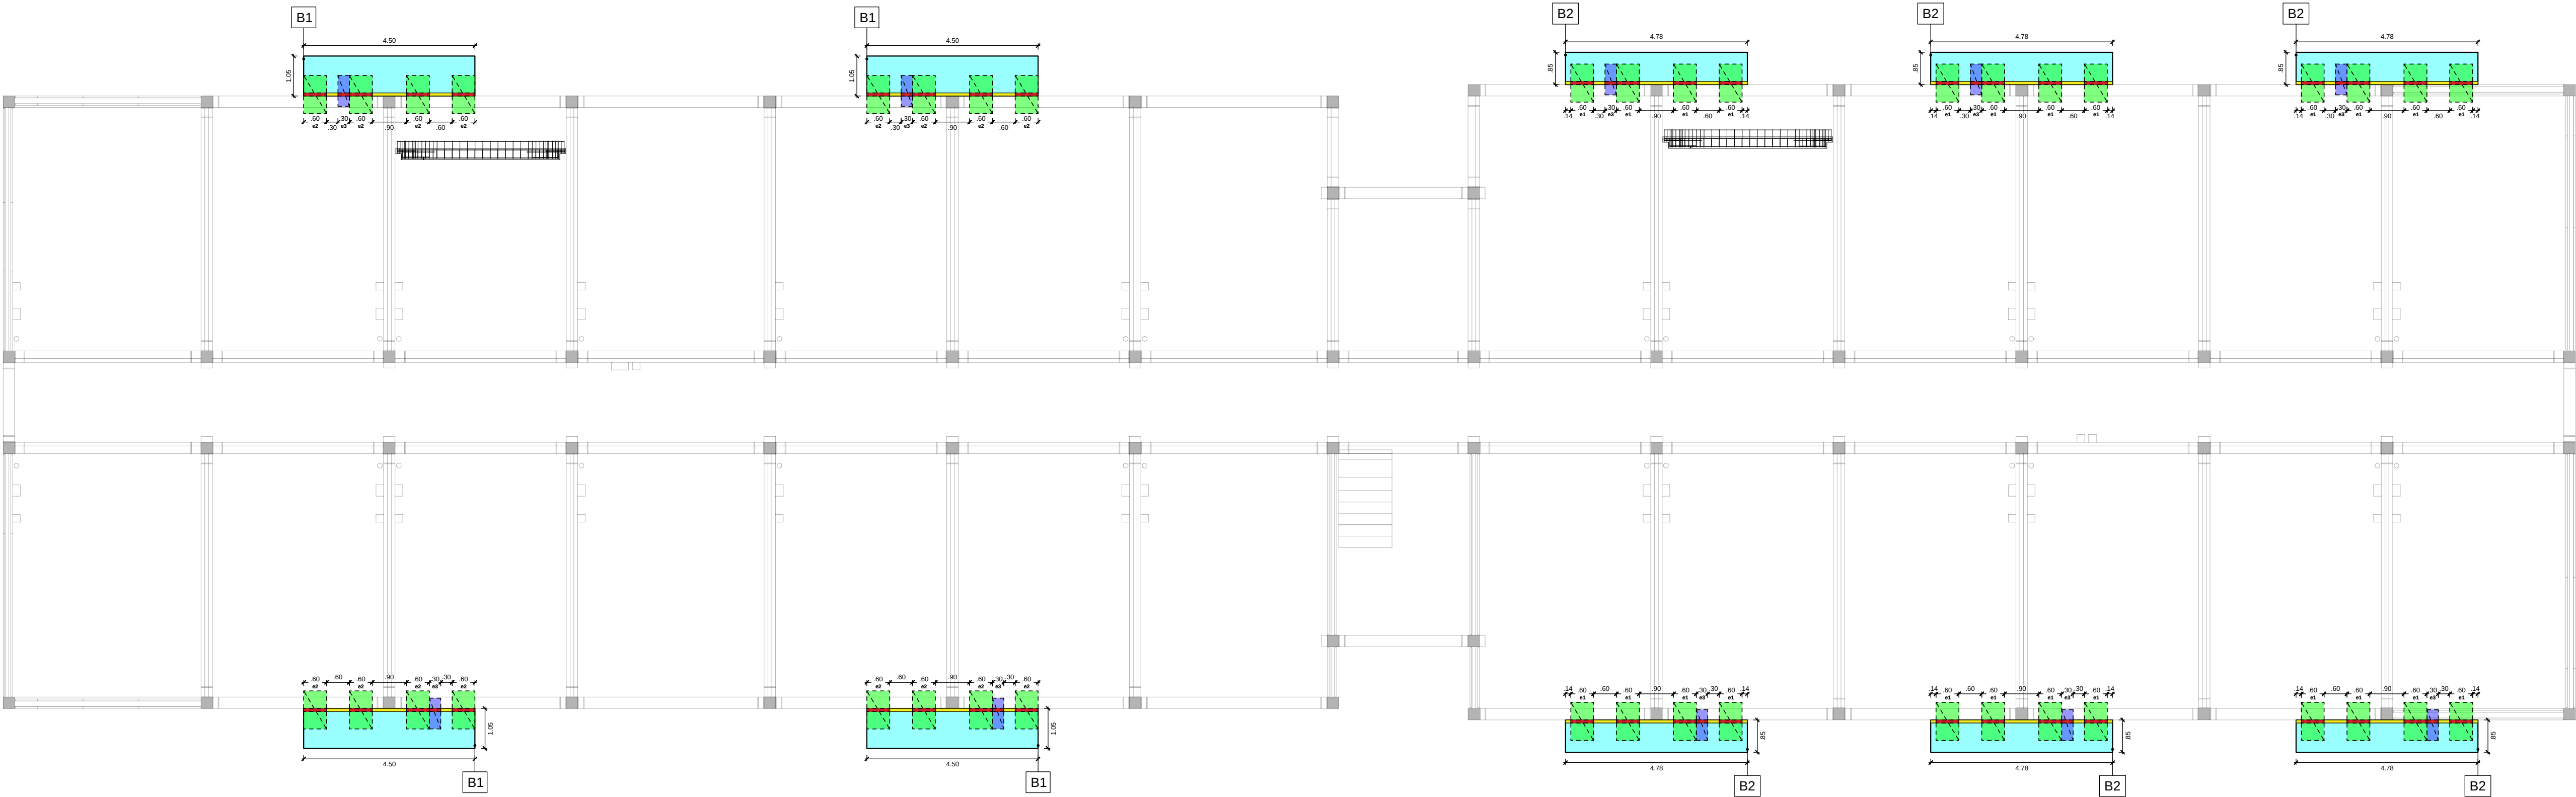

Megjegyzések:

1. Az elemek beépítése kizárólag a felelős statikus tervező részbeli jóváhagyása mellett történhet. Az elemek teherbíróssága a katalógusban megtalálható. A felüntetett teherbírósságok C25/30-as betonminőségűre vonatkoznak.
2. A vasbeton szerkezeti elemek nem kerültek felvázolásra. Azok megfelelő vasalással történő ellátása a statikus tervező feladata. A vasbeton szerkezeti elemek méretezése során a hővezetési tényező elemek hatását figyelembe kell venni.
3. Az elemek beépítésénél a megrendelő elvárásait ellenőrizni kell. A megrendőssel az ajánlatban bemutatott műszaki megoldást elfogadják. Ezzel egyetemben a méreteket ellenőrizni szükséges.
4. Az ajánlat csak az összes melléklettel együtt érvényes.
5. A sárgával jelölt helyekre EBEA-ZS SW80 EI120 vagy egyenértékű szigetelőelem beépítése szükséges!

Termék: EBEA	Építési típus: Munkásszili	Lap: A3; M1:100
Verzió: R01	Építési cím: Nyregyháza	Dátum: 07.09.2026
	Szállítási cím: Takács Cédő	Projektazonosító: HU2317
	Kezítő: keztibó	Tervező: S1